


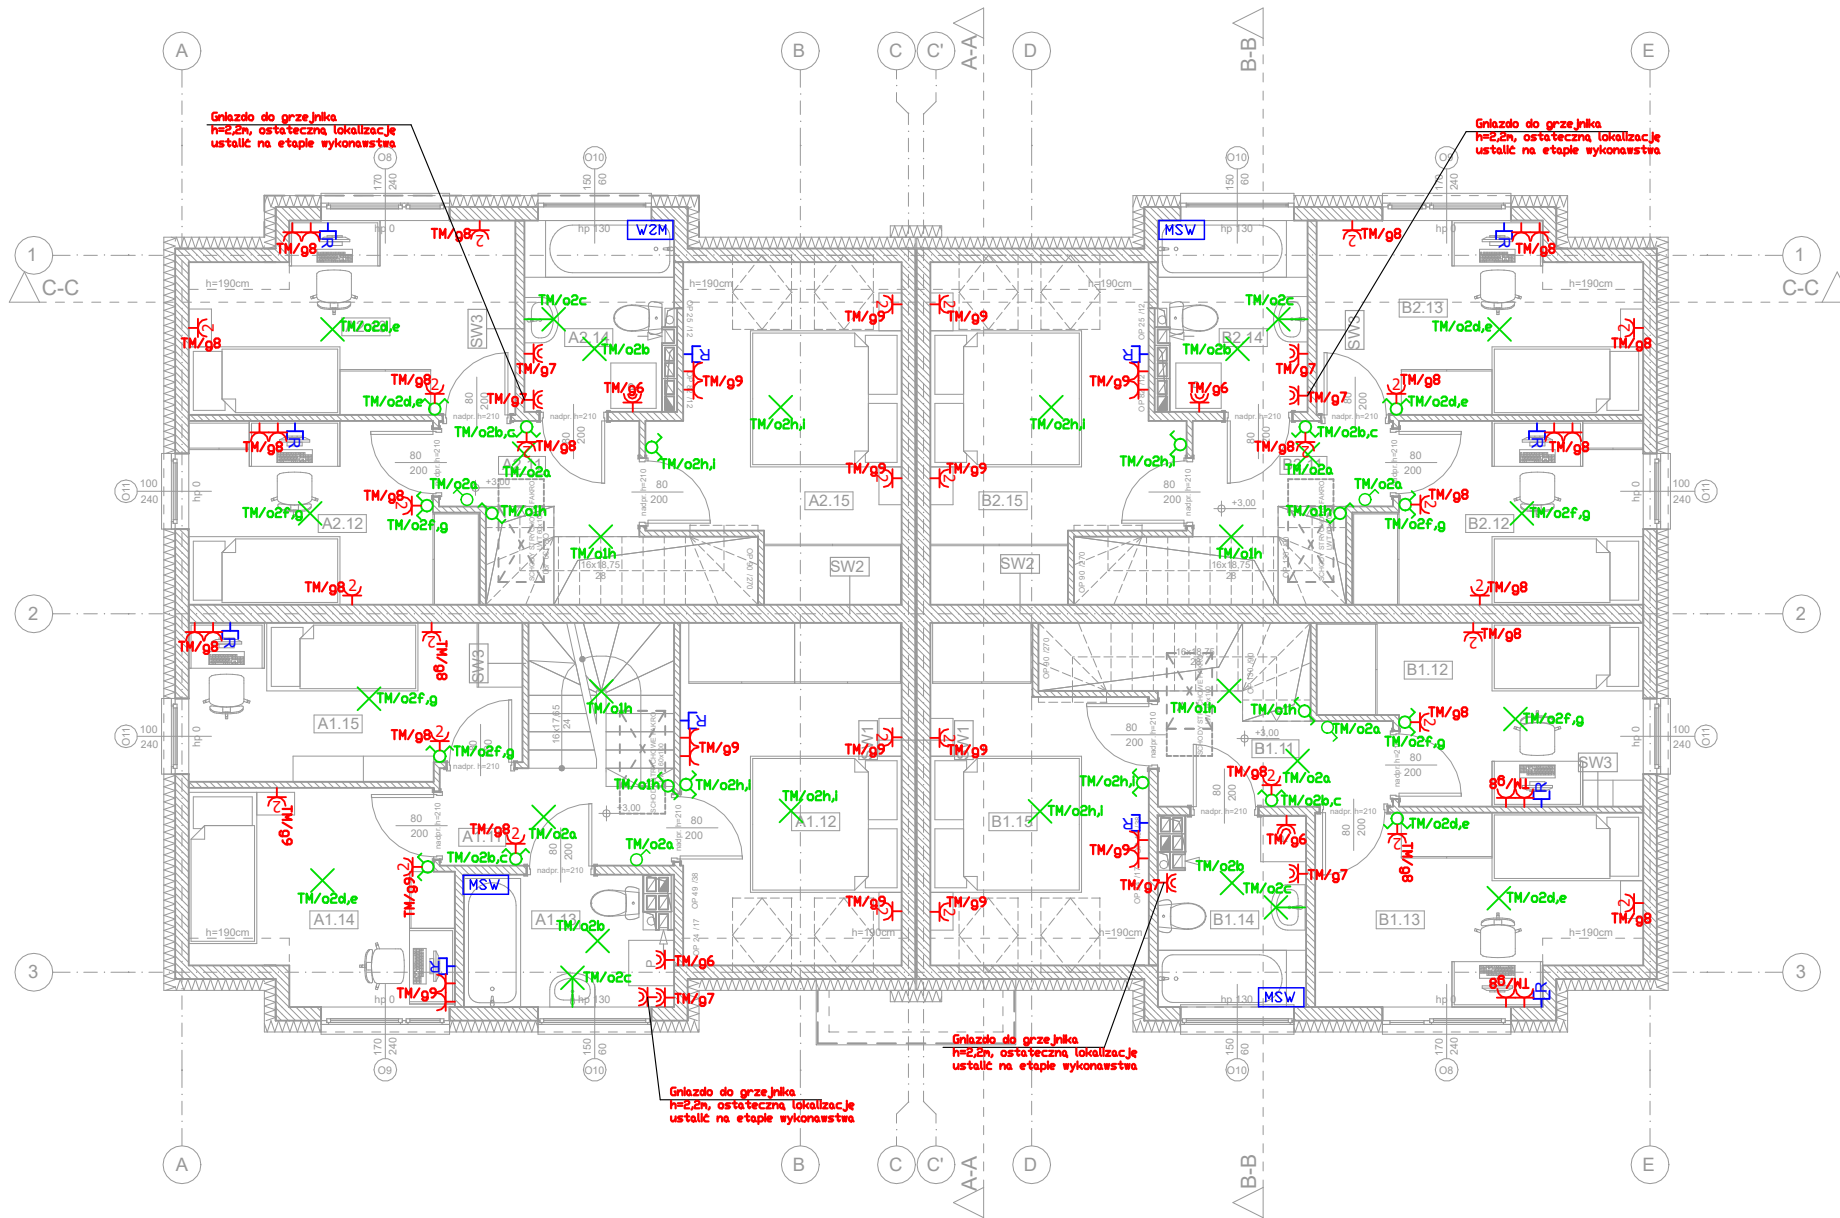

- LEGENDA:
- TM rozdzielnica główna mieszkaniowa
 - TAB rozdzielnica administracyjna budynku
 - TSM teletechniczna skrzynka mieszkaniowa
 - GSW główna szyna wyrównawcza
 - MSW lokalna(miejskowa) szyna wyrównawcza
 - ~ gniazdo 230V pojedyncze z uziemieniem,
 - ~ gniazdo 230V podwójne z uziemieniem,
 - 400V wypust 400V zasilanie kuchenki zakończony puszką n/t
 - ~ gniazdo 230V pojedyncze z uziemieniem, bryzgoszczelne,
 - ~ łącznik schodowy
 - ~ łącznik jednobiegunowy
 - ~ łącznik świecznikowy
 - ~ wypust oświetleniowy sufitowy
 - ~ wypust oświetleniowy ścienny
 - A oprawa oświetleniowa z czujnikiem ruchu np. LOTOS ELEGANCE ROUND PC LED COMPACT V2 1800 E CMW IP54 840
 - B oprawa oświetleniowa np. PLAFOND SQUARE LED 2000 PC E IP54 840
 - INT gniazdo 2xRJ45 kat 5e
 - TV gniazdo TV 1xRG6
 - R orurowanie do TSM
 - ~ przycisk zwirny - dzwonek
 - ~ panel wywołania - wideodomofon
 - ~ unifon mieszkaniowy

NAZWA INWESTYCJI:			
BUDYNKI MIESZKALNE JEDNORODZINNE W ZABUDOWIE BLIŹNIACZEJ			
ADRES INWESTYCJI:			
ul. Zagórzeńska, Warszawa - Wawer, dz. ew. gr. nr 63/1-63/14, z obręb 3-15-03			
INWESTOR:			
			
		Albero Invest - 2 sp. z o.o. ul. Zielna 37, 00-108 Warszawa	
GŁÓWNY PROJEKTANT:			
		VERTIKAL DESIGN Sp. z o.o. ul. Janiszowska 14 02-264 Warszawa	
PROJEKTANT:		PODPIS:	
mgr inż. Emil Bursiewicz Nr upr. PDL/0159/PWBE/16 w spec. sieci i urządzeń elektrycznych			
OPRACOWANIE:			
mgr inż. Łukasz Jabłoński			
FAZA PROJEKTU:		BRANŻA:	
PROJEKT WYKONAWCZY		ELEKTRYCZNA	
TYTUŁ RYSUNKU:			
RZUT PIĘTRA - INSTALACJE ELEKTRYCZNE			
NR RYSUNKU:		REWIZJA:	
PW_E_02		REV. 2	
NR PROJEKTU:	DATA:	FORMAT:	SKALA:
VD_030	07.2021		1:100