


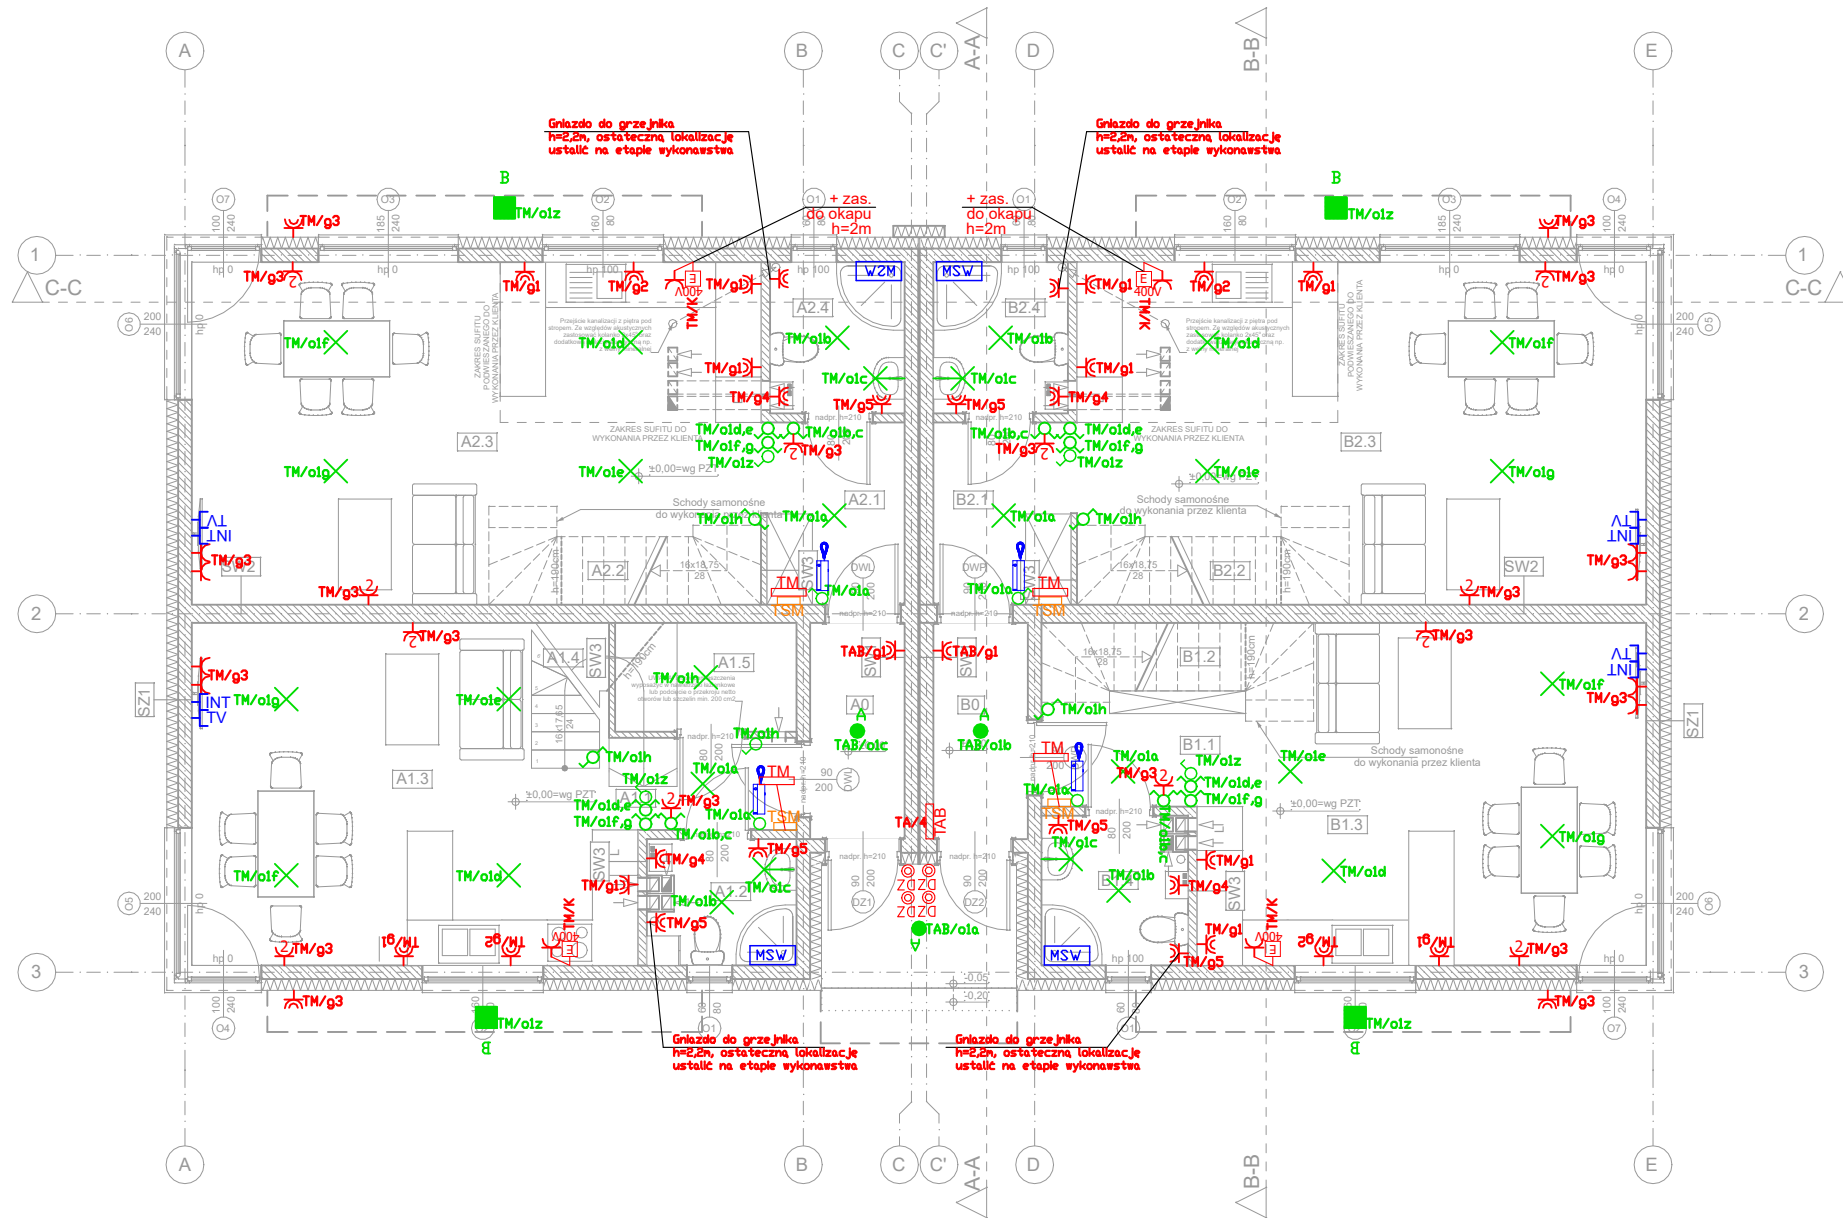

LEGENDA:

- TM** rozdzielnica główna mieszkaniowa
- TAB** rozdzielnica administracyjna budynku
- TSM** teletechniczna skrzynka mieszkaniowa
- GSW** główna szyna wyrównawcza
- MSW** lokalna(miejskowa) szyna wyrównawcza
- gniazdo 230V pojedyncze z uziemieniem,
- gniazdo 230V podwójne z uziemieniem,
- wypust 400V zasilanie kuchenki zakończony puszką n/t
- gniazdo 230V pojedyncze z uziemieniem, brygoszczelne,
- łącznik schodowy
- łącznik jednobiegunowy
- łącznik świecznikowy
- wypust oświetleniowy sufitowy
- wypust oświetleniowy ścienny
- oprawa oświetleniowa z czujnikiem ruchu np. LOTOS ELEGANCE ROUND PC LED COMPACT V2 1800 E CMW IP54 840
- oprawa oświetleniowa np. PLAFOND SQUARE LED 2000 PC E IP54 840
- gniazdo 2xRJ45 kat 5e
- gniazdo TV 1xRG6
- orurowanie do TSM
- przycisk zwirny - dzwonek
- panel wywołania - wideodomofon
- unifon mieszkaniowy

NAZWA INWESTYCJI: BUDYNKI MIESZKALNE JEDNORODZINNE W ZABUDOWIE BLIŹNIACZEJ			
ADRES INWESTYCJI: ul. Zagórzeńska, Warszawa - Wawer, dz. ew. gr. nr 63/1-63/14, z obrębu 3-15-03			
INWESTOR:  Albero Invest - 2 sp. z o.o. ul. Zielna 37, 00-108 Warszawa			
GŁÓWNY PROJEKTANT:  VERTIKAL DESIGN Sp. z o.o. ul. Janiszowska 14 02-264 Warszawa			
PROJEKTANT: mgr inż. Emil Bursiewicz Nr upr. PDL/0159/PWBE/16 w spec. sieci i urządzeń elektrycznych		PODPIS:	
OPRACOWANIE: mgr inż. Łukasz Jabłoński			
FAZA PROJEKTU: PROJEKT WYKONAWCZY		BRANŻA: ELEKTRYCZNA	
TYTUŁ RYSUNKU: RZUT PARTERU - INSTALACJE ELEKTRYCZNE			
NR RYSUNKU: PW_E_01		REWIZJA: REV. 2	
NR PROJEKTU: VD_030	DATA: 07.2021	FORMAT:	SKALA: 1:100